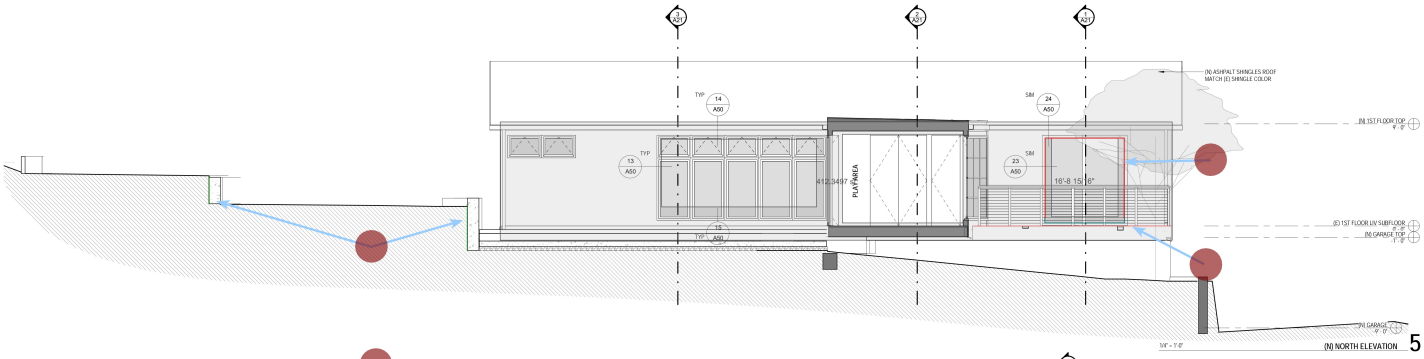

(N) NORTH ELEVATION 5

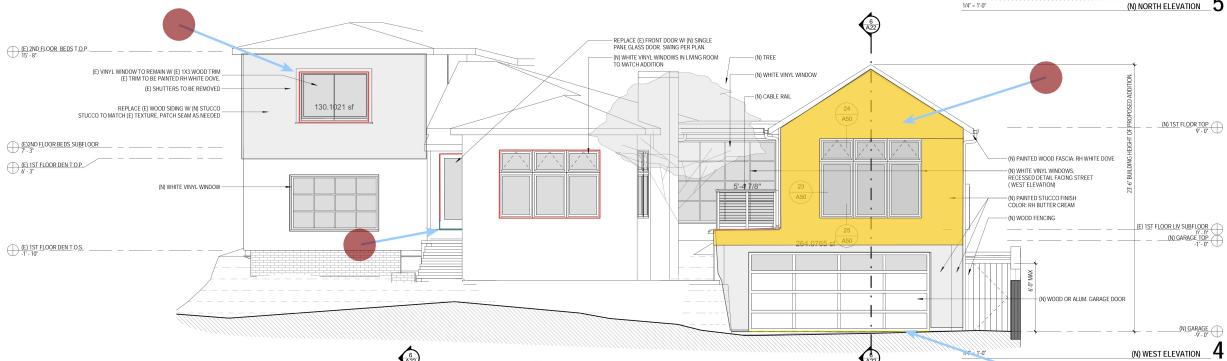

(N) WEST ELEVATION 4

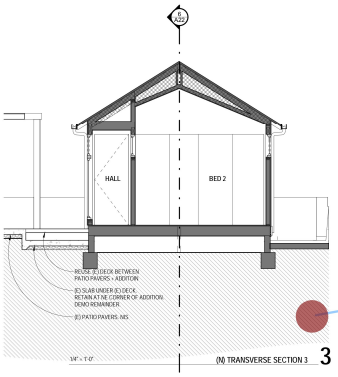

(N) TRANSVERSE SECTION 3 3

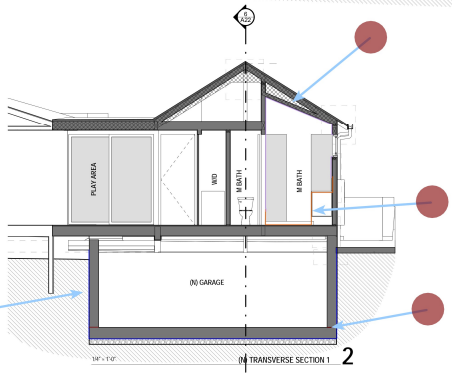

(N) TRANSVERSE SECTION 1 2

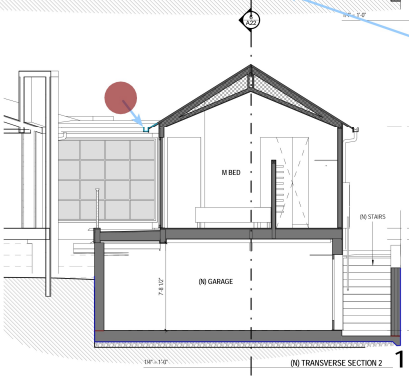

(N) TRANSVERSE SECTION 2 1

Nina + Gordana

N+G

2048 Vine Street, Paso Robles, CA 93446
650.888.8933 | nasarov ninar@gmail.com

602 Hawthorne Ave, Palo Alto, CA 94301
650.493.4422 | design@gordana.net

STALEY RESIDENCE ADDITION

2408 San Carlos Ave, San Carlos, CA

DATE: 31 JANUARY 2019

REVISIONS:

(N) ELEVATIONS + SECTIONS

A21